

D

C

B

A




D

C


B

A

REV	DESCRIPTION	DRAWN BY:	DATE
2X	34.50 IMPEL CUTOUT HEIGHT WAS 35.00 (SHEET 2).	R. GRANTHAM, 6/23/22	

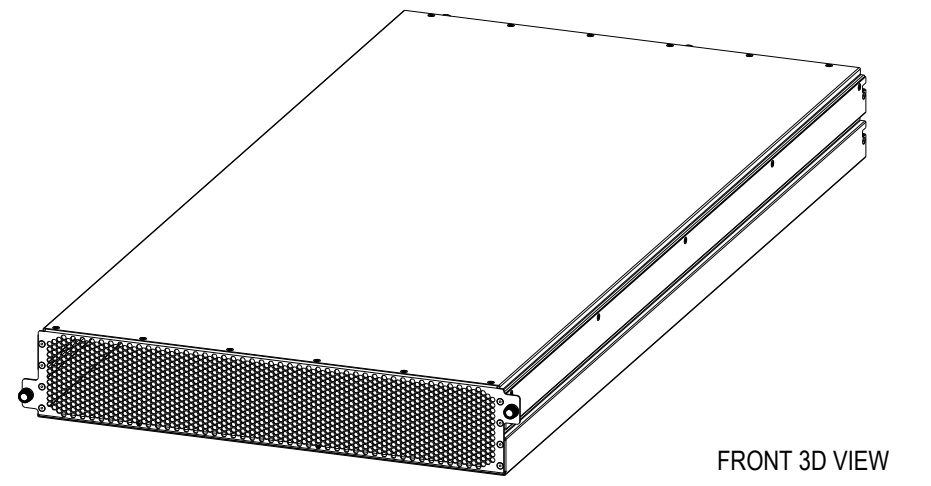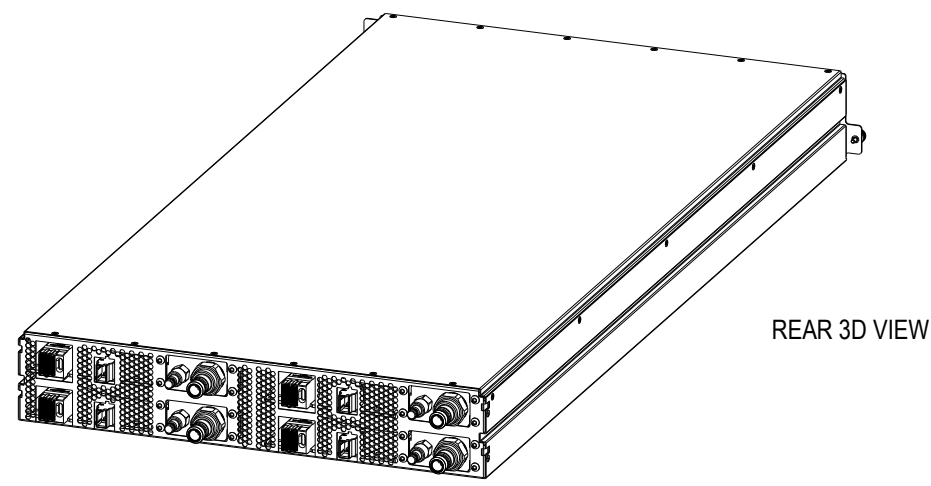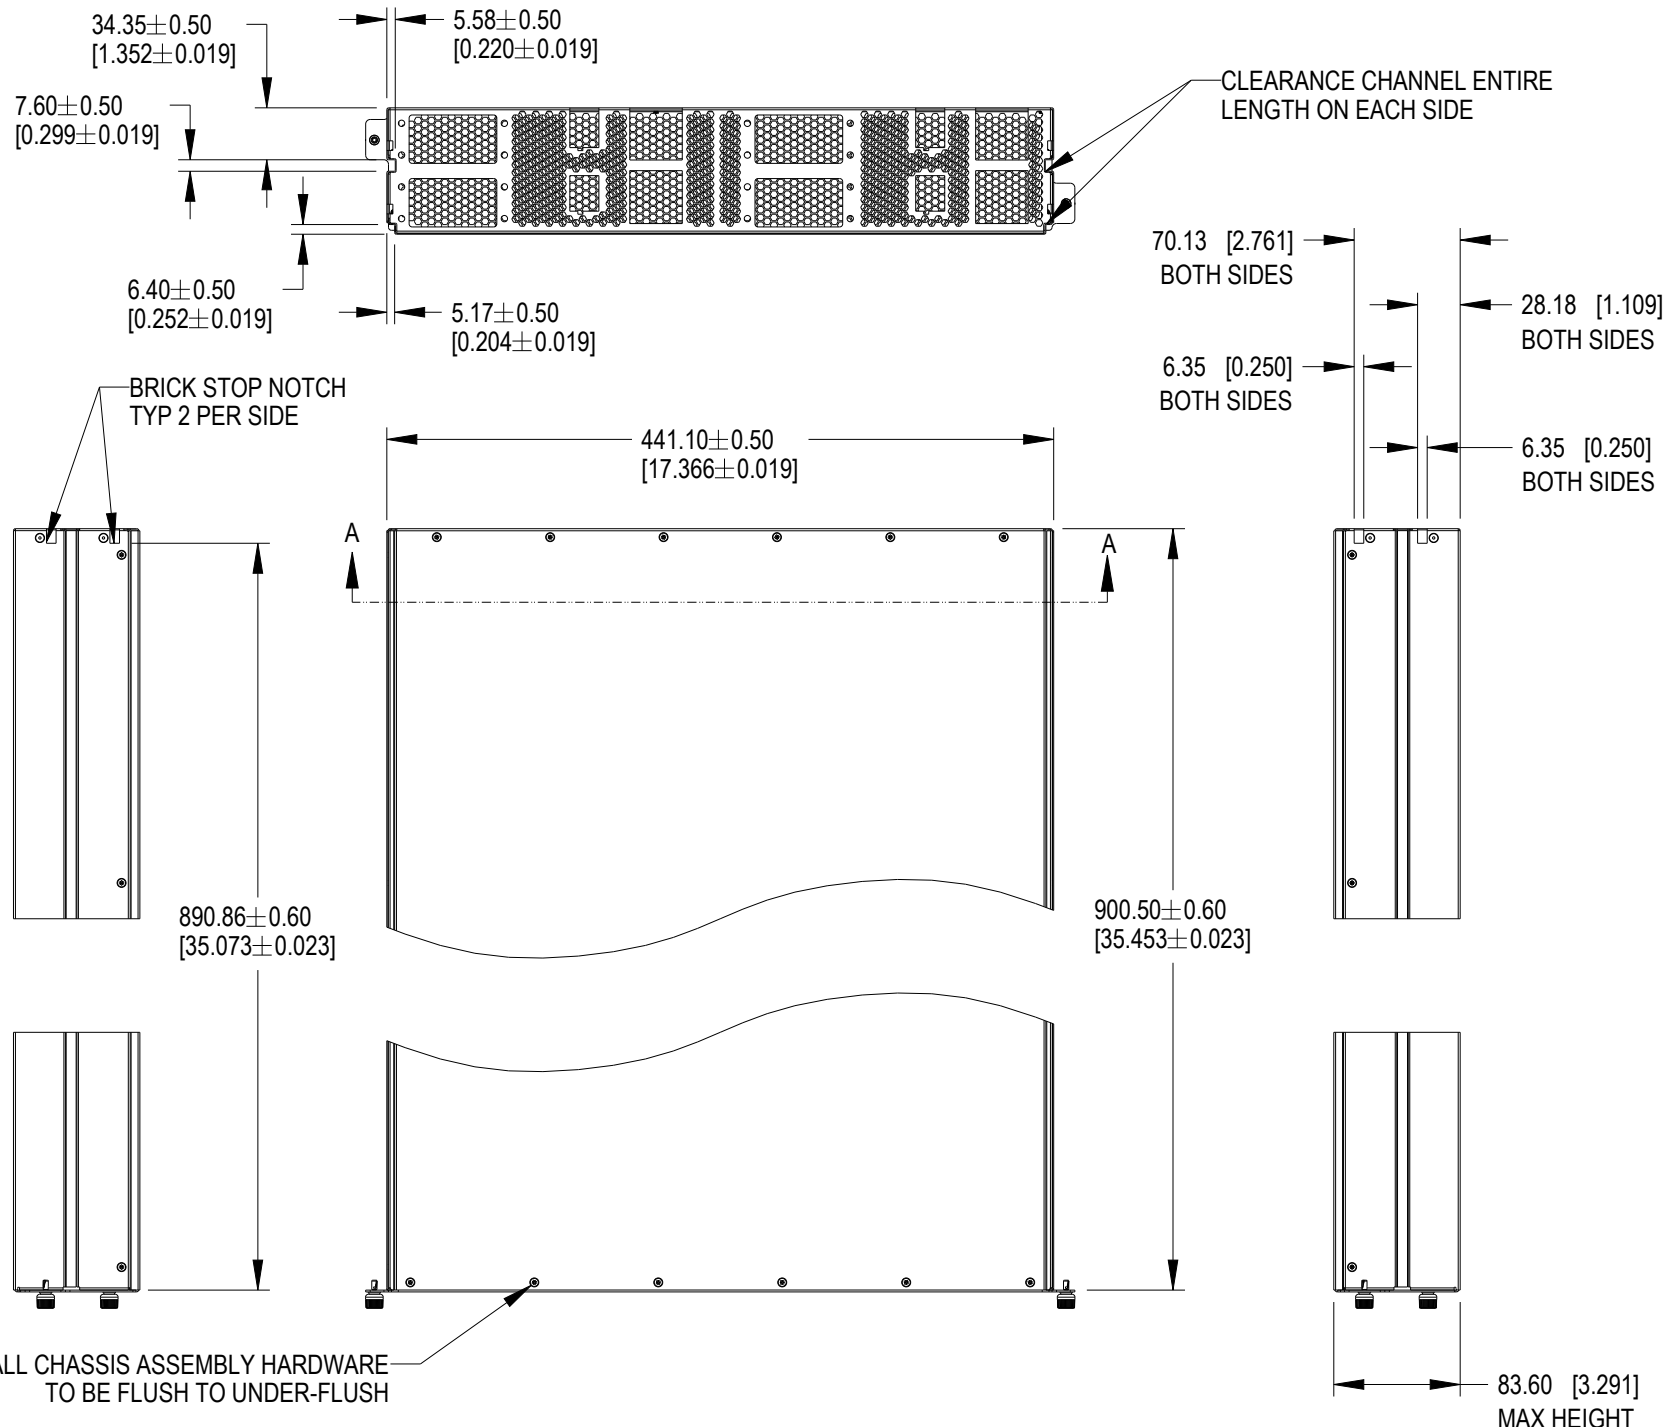

MATERIAL:			UNLESS OTHERWISE SPECIFIED TOLERANCE				OPEN 19		
NONE			MM (PRIMARY) INCHES (SECONDARY)						
FINISH:			X ± 2 (X) ± 1						
NONE			X ± 8 (XX) ± 03						
DESIGNED BY:			DATE:		WEIGHT:		PART DESCRIPTION		
R. GRANTHAM			14 FEB 2022		-				
DRAWN BY:			DATE:		SHEET:				
R. GRANTHAM			17 JUN 2022		1/3				
THIRD ANGLE PROJECTION			SIZE		SCALE		DOCUMENT NUMBER		
C			B		0.200		OPEN19 2W2H BRICK		
REV			REV		REV		REV		
2X			1/3		2X		2X		

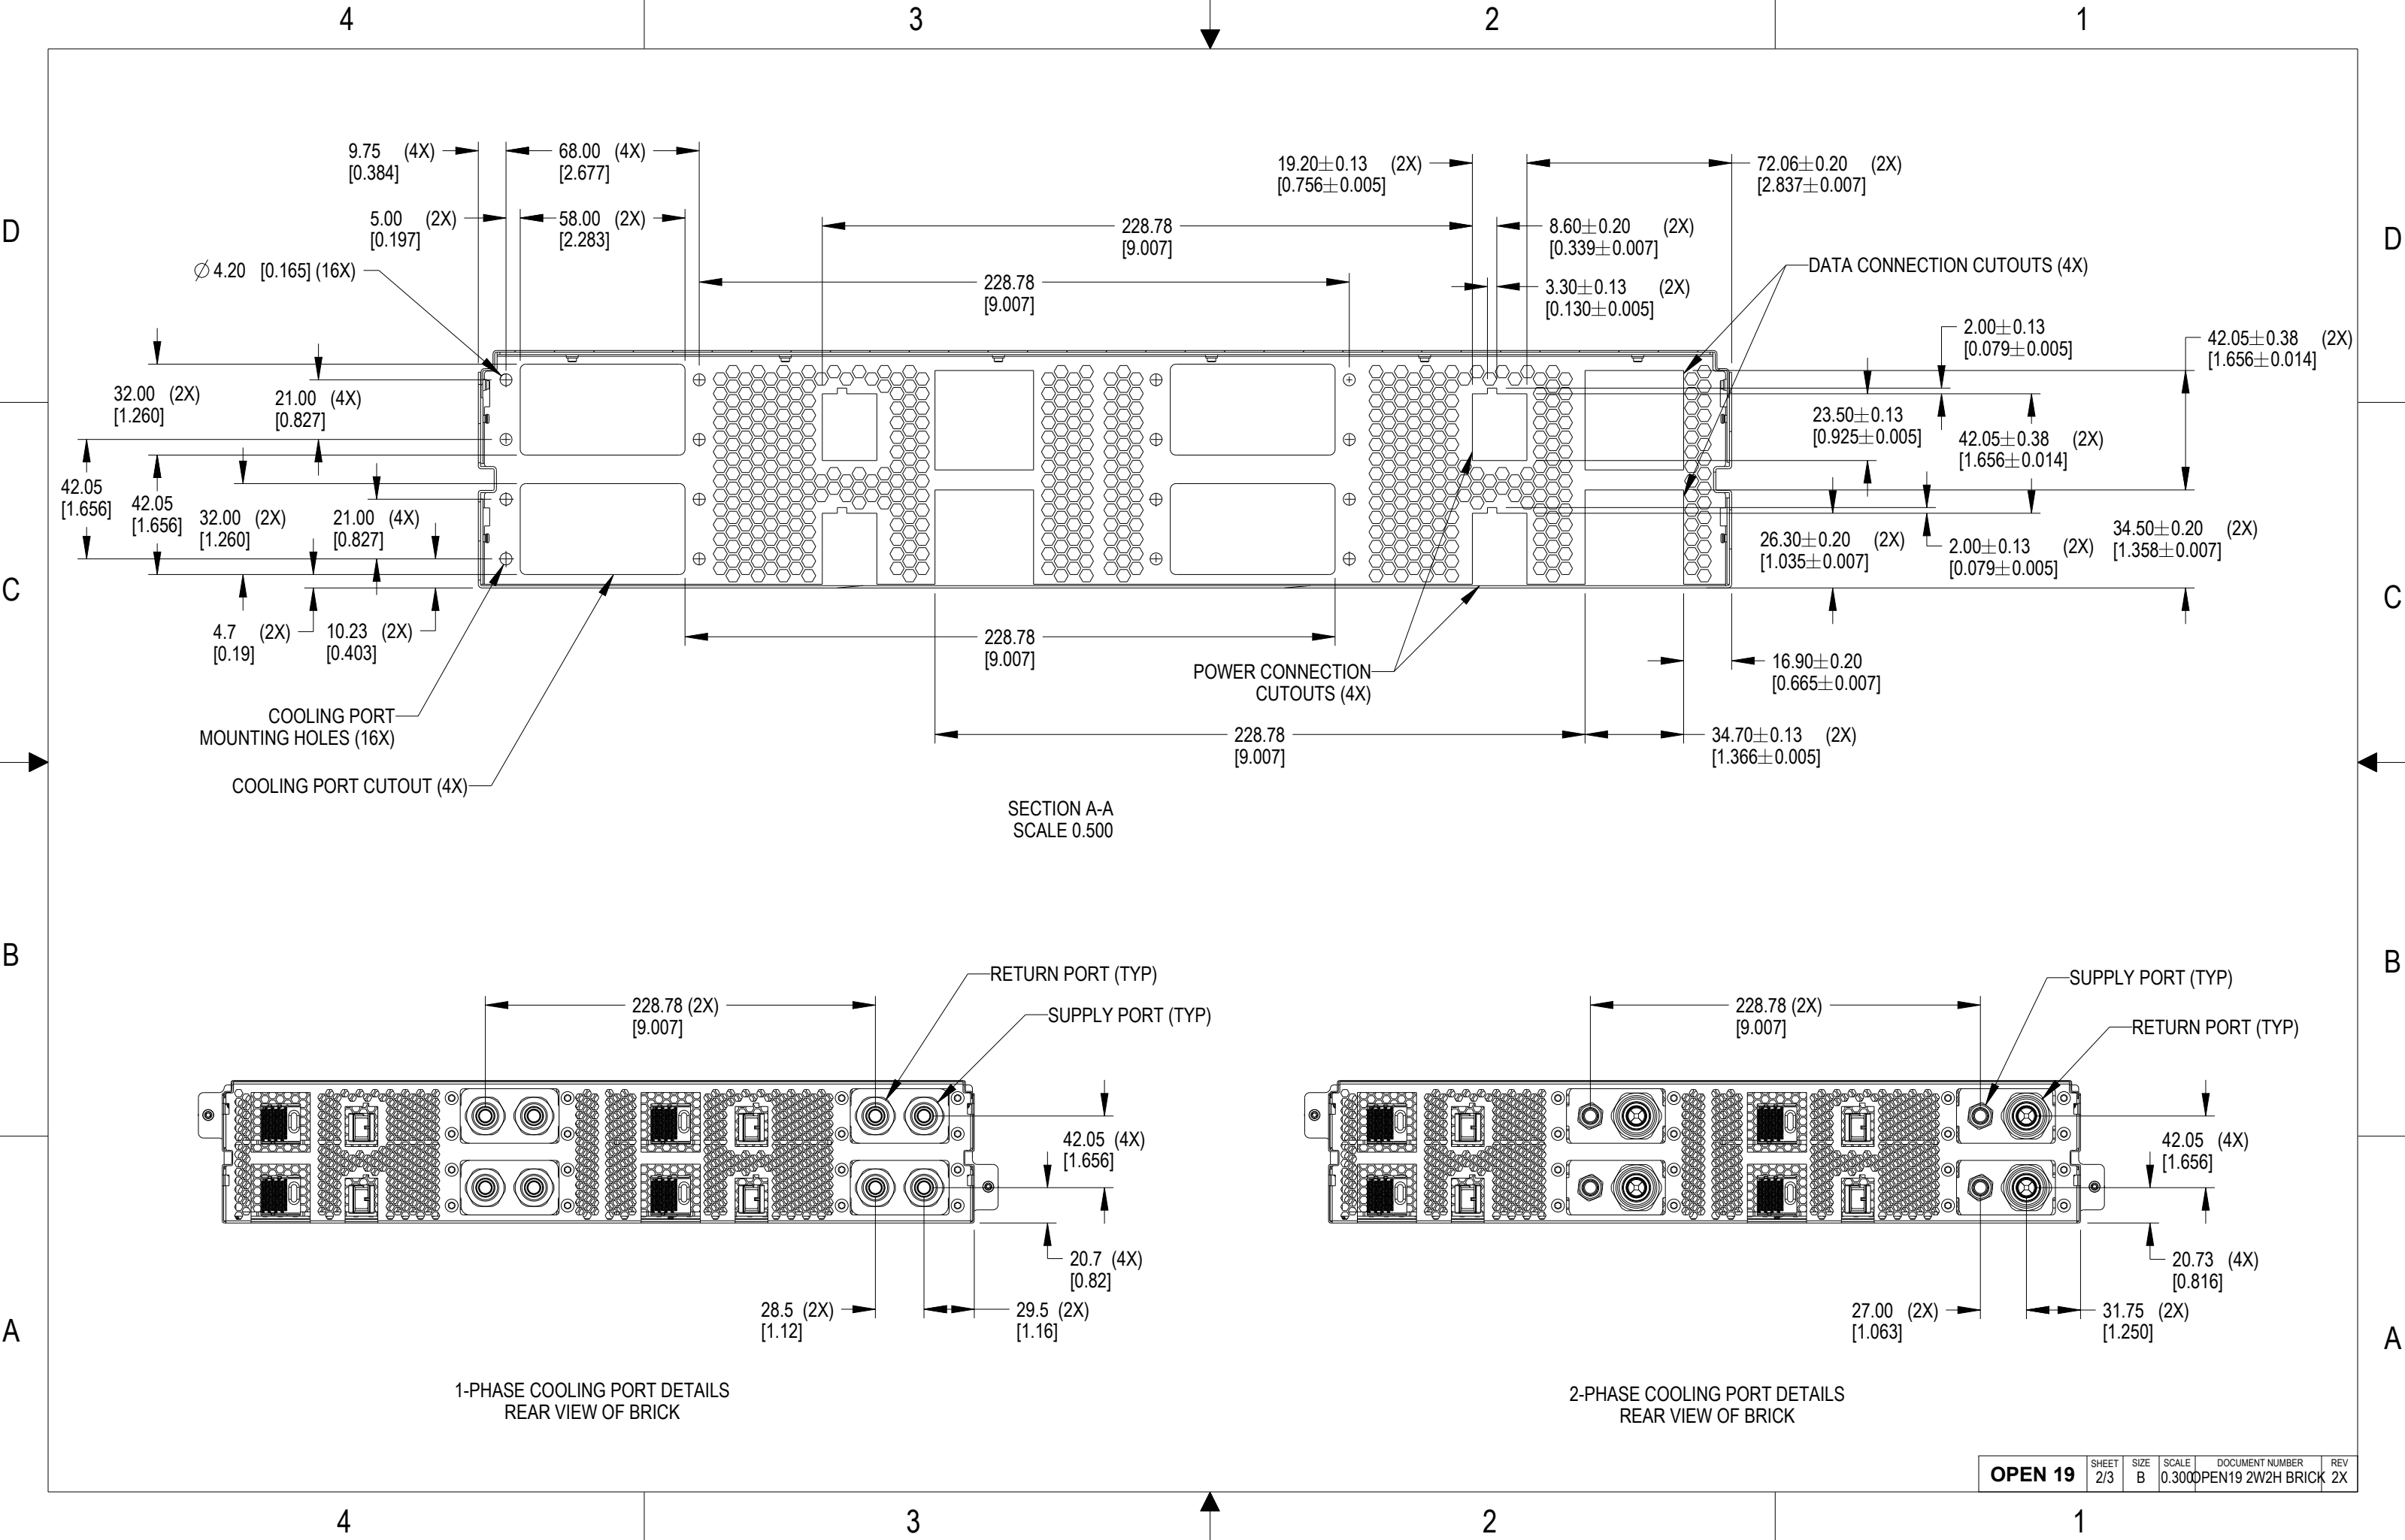

D

C

B





A

D

C

B

A

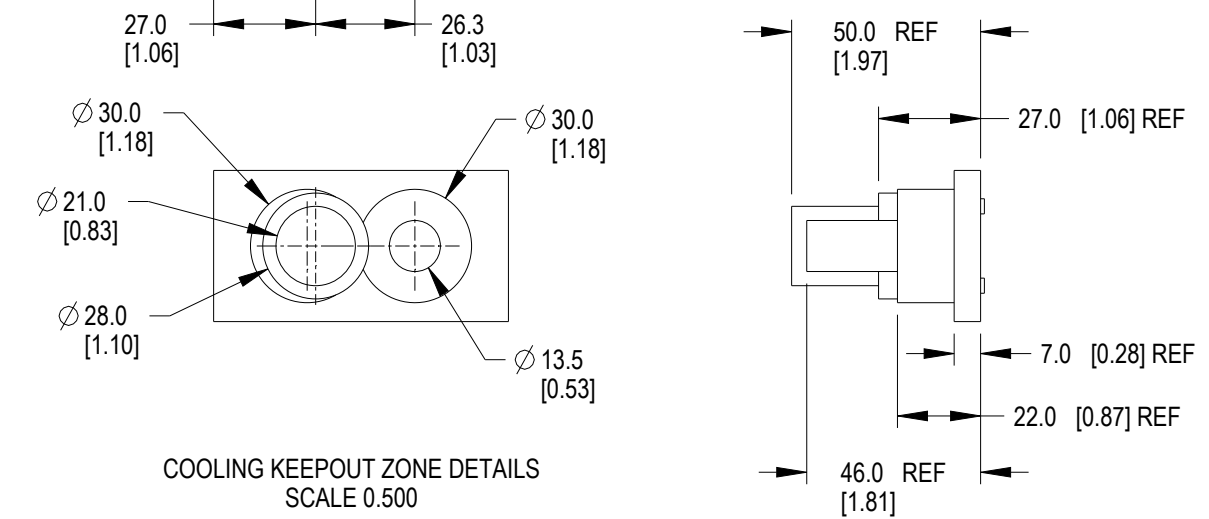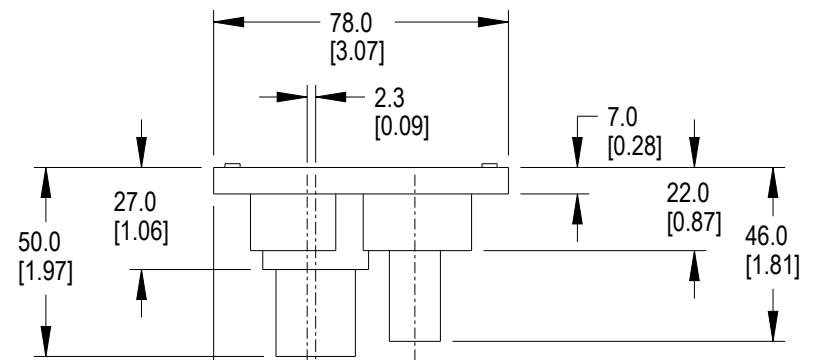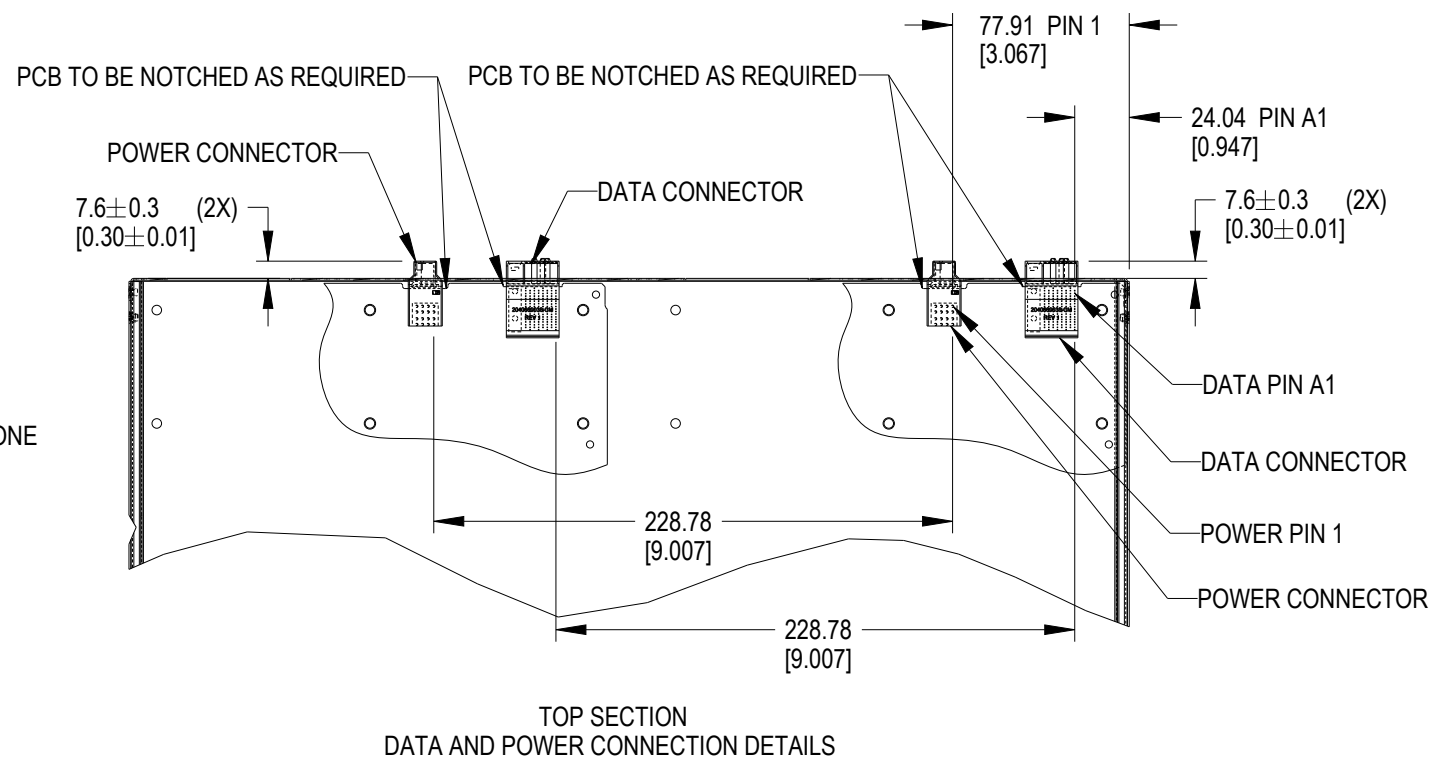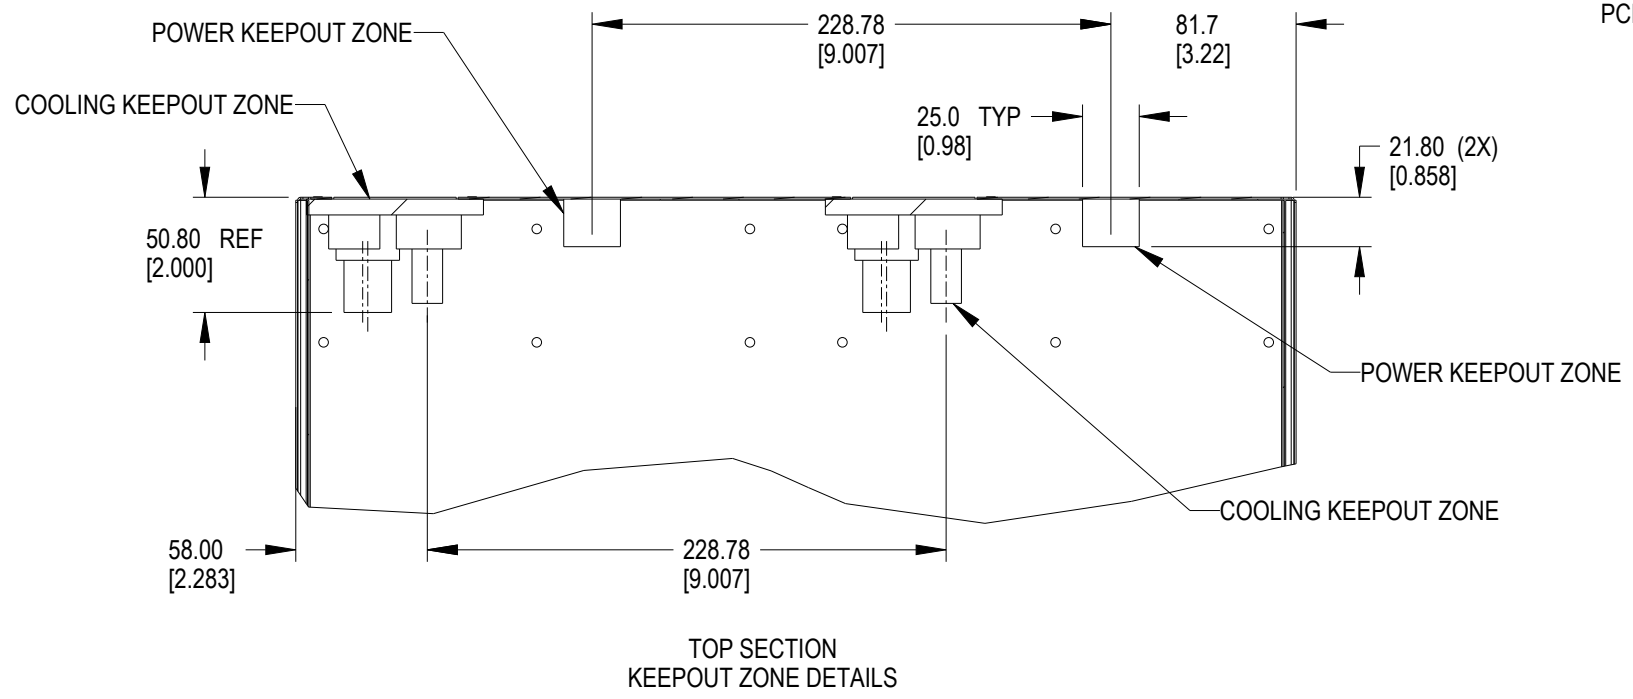

ELECTRICAL CONNECTIONS DETAIL
REAR VIEW OF BRICK

